

KEY PLAN

SCALE 1:1,500,000

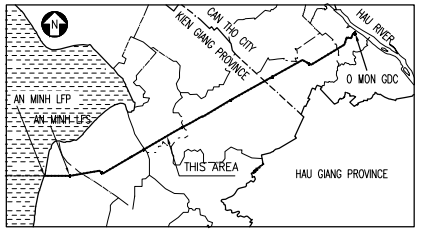

WELD MAP

FROM KP 36.000 TO KP 37.000

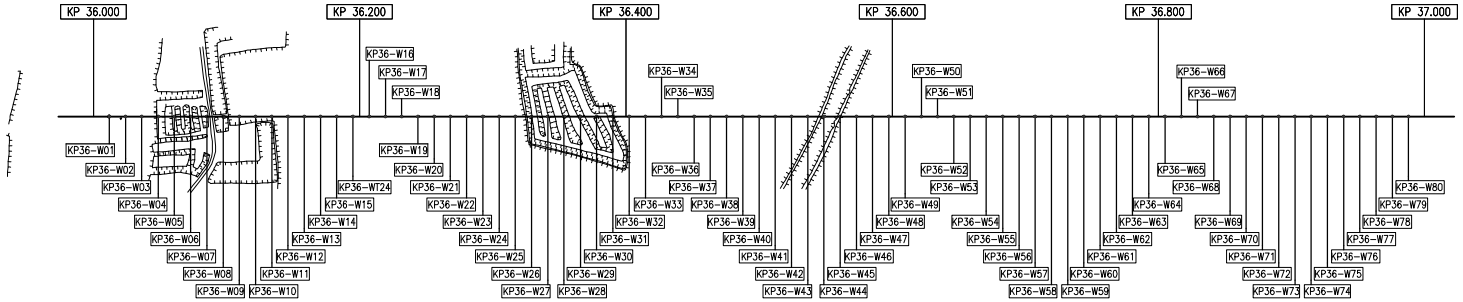

NOTE:

KP....-Wxx: Welding Joint Number

WPS: SWG-PTSCL18-WPS-PL-30-01/SWG-PTSCL18-WPS-PL-30-02

100% AUT or RT for Butt Joint

Material information

+ Pipe: API 5L X65M PSL2 OD 762mm x 19.1mm

POND, DITCH, CANNAL

DIRT ROAD

M.S.D.N:0300390921-C.T.C.P
CÔNG TY CỔ PHẦN LILAMA 18
P.SÀI GÒN - T.P HỒ CHÍ MINH

PHÓ TỔNG GIÁM ĐỐC
NGUYỄN KHẮC THÀNH

APPROVED FOR CONSTRUCTION

REV.	DATE	DESCRIPTION	DRAW	CHECK	REW'D	APP
0	28/01/26	ISSUED FOR APPROVAL	NTT	LTV	PTG	HAV

CLIENT: VIETNAM NATIONAL INDUSTRY - ENERGY GROUP
SOUTHWEST PIPELINE OPERATING COMPANY

EPC CONTRACTOR: PTSC-LILAMA 18 CONSORTIUM

PROJECT: **BLOCK B - O MON GAS PIPELINE**
STAGE: CONSTRUCTION


TITLE: ONSHORE PIPELINE WELD MAP
FROM KP36 +000 TO KP37 +000

SCALE	DRAWING NO	SHEET
NA	SWG-PTSCL18-CON-70-PL-WMP-0002	30/94

A3 (420x297mm)


KEY PLAN

SCALE 1:1,500,000

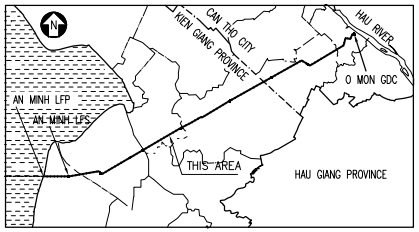

WELD MAP

FROM KP 37.000 TO KP 38.000

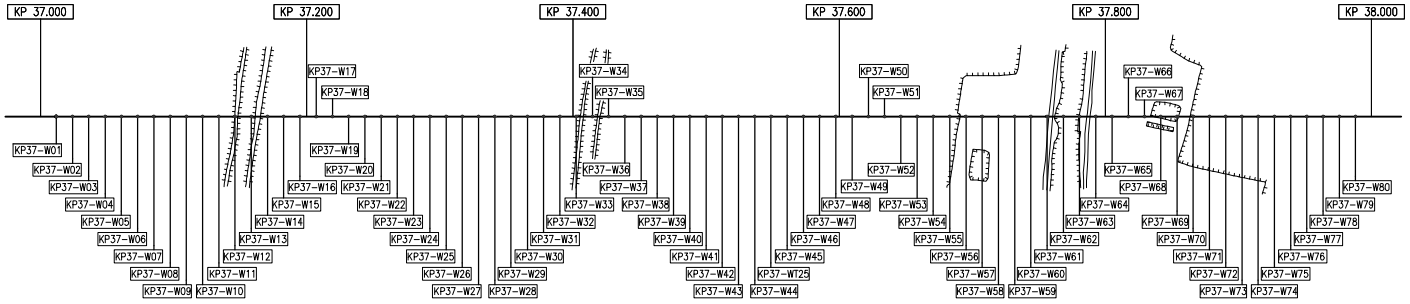

NOTE:

KP....-Wxx: Welding Joint Number

WPS: SWG-PTSCL18-WPS-PL-30-01/SWG-PTSCL18-WPS-PL-30-02

100% AUT or RT for Butt Joint

Material information

+ Pipe: API 5L X65M PSL2 OD 762mm x 19.1mm

POND, DITCH, CANNAL

DIRT ROAD

M.S.D.N: 0300398927 - C.T.C.P
CÔNG TY CỔ PHẦN LILAMA 18
P. SÀI GÒN - T.P HỒ CHÍ MINH

PHÓ TỔNG GIÁM ĐỐC
NGUYỄN KHẮC THÀNH

APPROVED FOR CONSTRUCTION

REV.	DATE	DESCRIPTION	DRAW	CHECK	REW'D	APP
0	28/01/26	ISSUED FOR APPROVAL	NTT	LTV	PTG	HAV

CLIENT: VIETNAM NATIONAL INDUSTRY - ENERGY GROUP
SOUTHWEST PIPELINE OPERATING COMPANY

EPC CONTRACTOR: PTSC-LILAMA 18 CONSORTIUM

PROJECT: **BLOCK B - O MON GAS PIPELINE**
STAGE: CONSTRUCTION


TITLE: ONSHORE PIPELINE WELD MAP
FROM KP37 +000 TO KP38 +000

SCALE	DRAWING NO	SHEET
NA	SWG-PTSCL18-CON-70-PL-WMP-0002	31/94

A3 (420x297mm)


KEY PLAN

SCALE 1:1,500,000

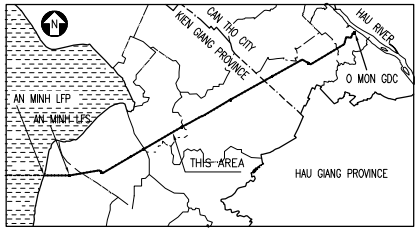

WELD MAP

FROM KP 38.000 TO KP 39.000

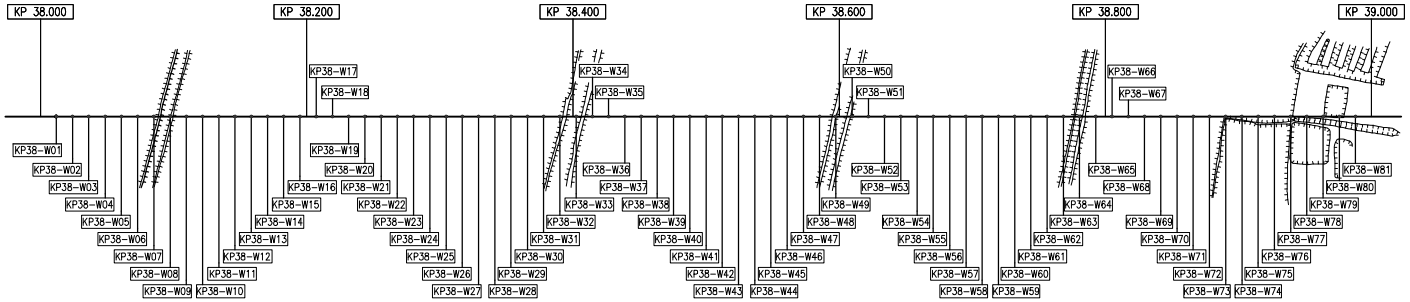

NOTE:

KP....–Wxx: Welding Joint Number

WPS: SWG–PTSCL18–WPS–PL–30–01/SWG–PTSCL18–WPS–PL–30–02

100% AUT or RT for Butt Joint

Material information

+ Pipe: API 5L X65M PSL2 OD 762mm x 19.1mm

POND, DITCH, CANNAL

DIRT ROAD

M.S.D.N: 0300390921 - C.T.C.P
CÔNG TY CỔ PHẦN LILAMA 18
P. SÀI GÒN - T.P HỒ CHÍ MINH

PHÓ TỔNG GIÁM ĐỐC
NGUYỄN KHẮC THÀNH

APPROVED FOR CONSTRUCTION

REV.	DATE	DESCRIPTION	DRAW	CHECK	REW'D	APP
0	28/01/26	ISSUED FOR APPROVAL	NTT	LTV	PTG	HAV

CLIENT: VIETNAM NATIONAL INDUSTRY - ENERGY GROUP
SOUTHWEST PIPELINE OPERATING COMPANY

EPC CONTRACTOR: PTSC-LILAMA 18 CONSORTIUM

PROJECT: **BLOCK B - O MON GAS PIPELINE**
STAGE: CONSTRUCTION


TITLE: ONSHORE PIPELINE WELD MAP
FROM KP38 +000 TO KP39 +000

SCALE	DRAWING NO	SHEET
NA	SWG–PTSCL18–CON–70–PL–WMP–0002	32/94

A3 (420x297mm)

WELD MAP

FROM KP 39.000 TO KP 40.000

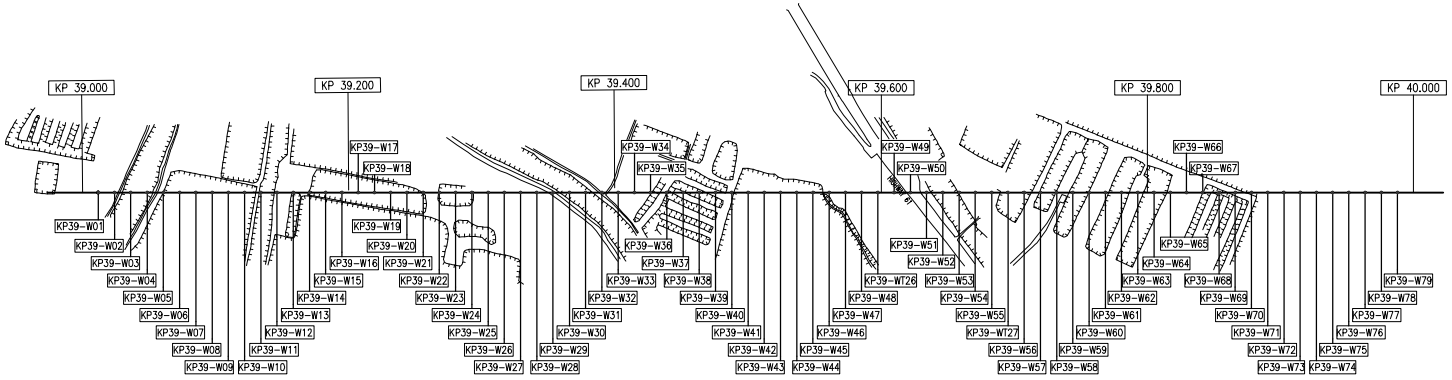

NOTE:

KP....-Wxx: Welding Joint Number

WPS: SWG-PTSCL18-WPS-PL-30-01/SWG-PTSCL18-WPS-PL-30-02

100% AUT or RT for Butt Joint

Material information

+ Pipe: API 5L X65M PSL2 OD 762mm x 19.1mm

POND, DITCH, CANNAL

DIRT ROAD


M.S.D.N: 0300390921 - C.T.C.P
CÔNG TY CỔ PHẦN LILAMA 18
P. SÀI GÒN - T.P HỒ CHÍ MINH

PHÓ TỔNG GIÁM ĐỐC
NGUYỄN KHẮC THÀNH

APPROVED FOR CONSTRUCTION

KEY PLAN

SCALE 1:1,500,000

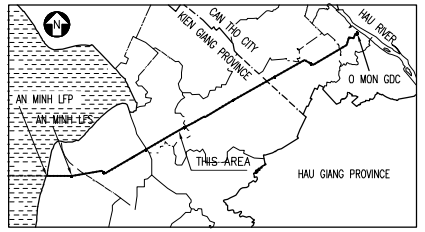

REV.	DATE	DESCRIPTION	DRAW	CHECK	REW'D	APP
0	28/01/26	ISSUED FOR APPROVAL	NTT	LTV	PTG	HAV

CLIENT: VIETNAM NATIONAL INDUSTRY - ENERGY GROUP
SOUTHWEST PIPELINE OPERATING COMPANY

EPC CONTRACTOR: PTSC-LILAMA 18 CONSORTIUM

PROJECT: **BLOCK B - O MON GAS PIPELINE**
STAGE: CONSTRUCTION

TITLE: ONSHORE PIPELINE WELD MAP
FROM KP39 +000 TO KP40 +000

SCALE	DRAWING NO	SHEET
NA	SWG-PTSCL18-CON-70-PL-WMP-0002	33/94

A3 (420x297mm)